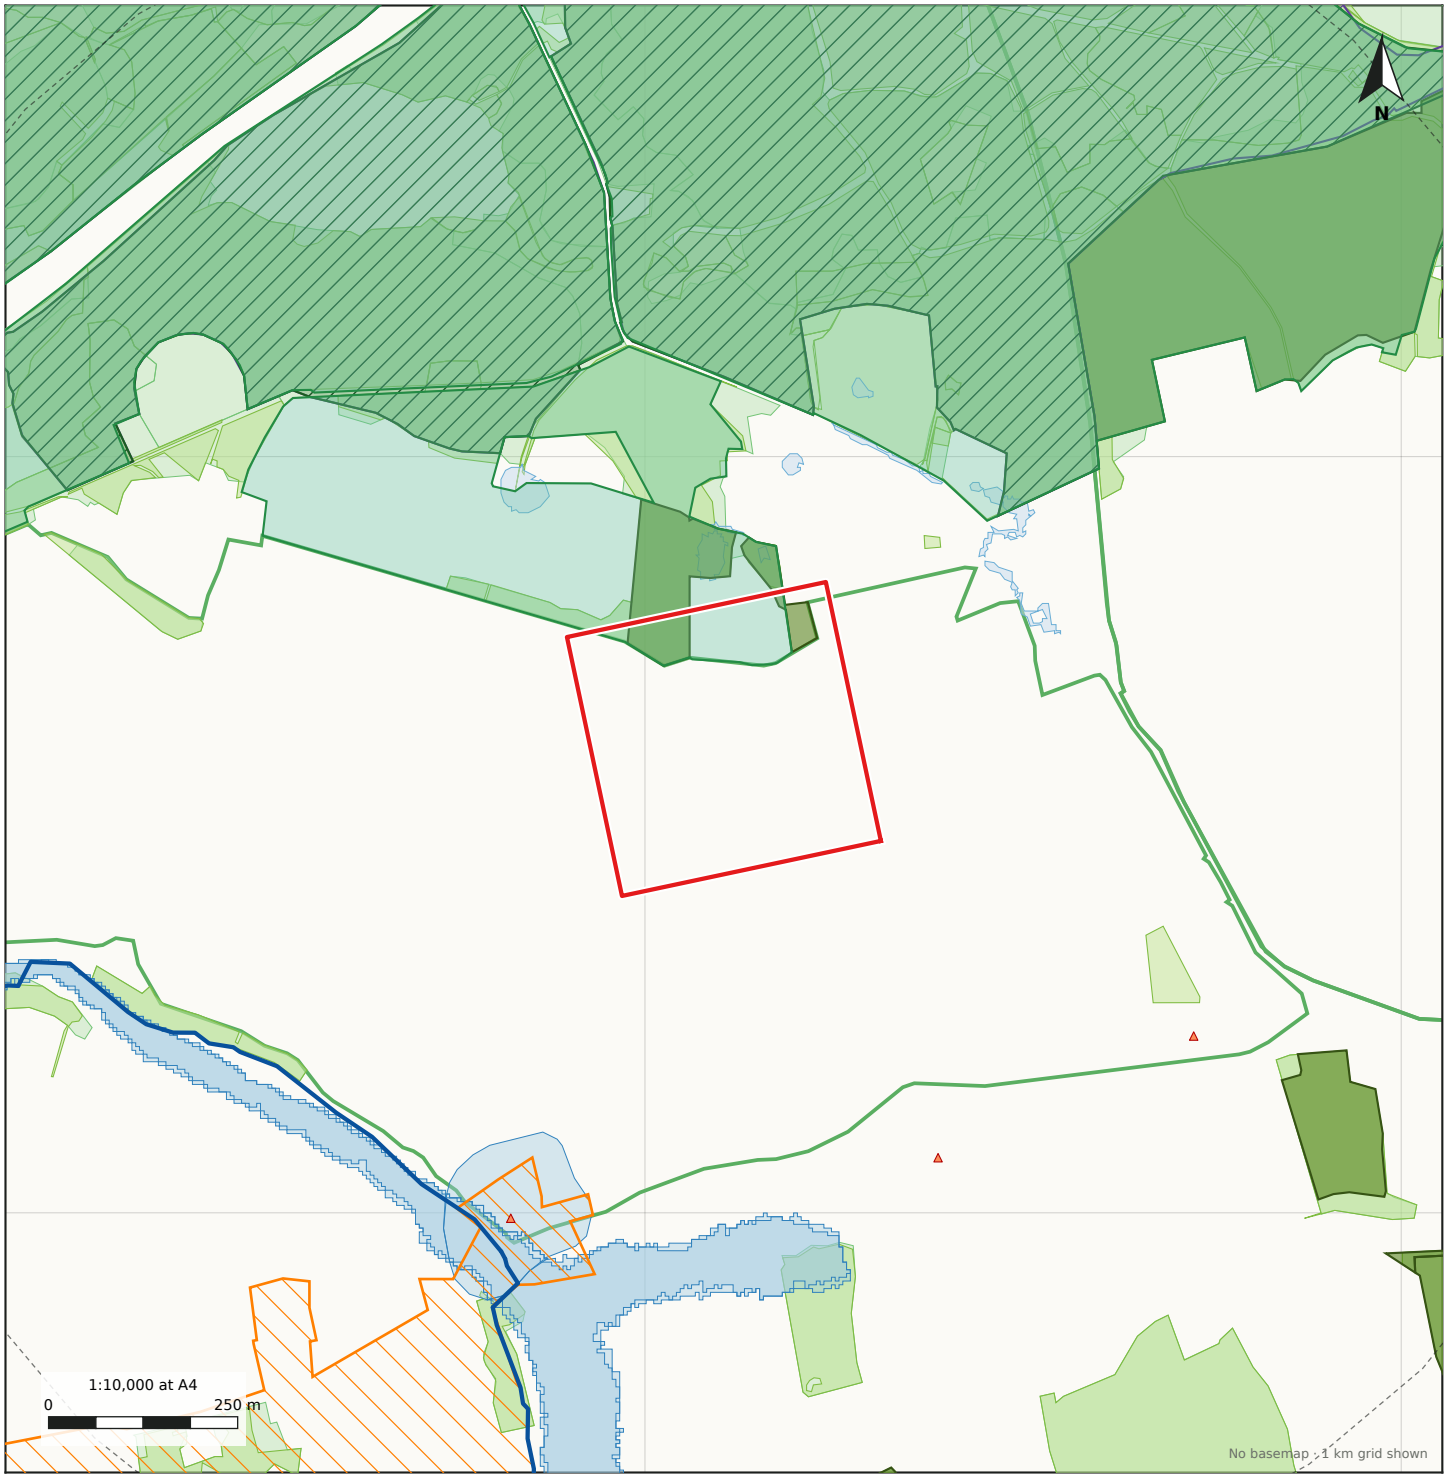


CONTOUR · DESK STUDY MAP

Former Wisley Airfield / Three Farms Meadows, Ockham

Red line 12.25 ha · centred 508,104 E, 157,627 N

TRIAL-wisley-airfield · 25 Oct 2026 19:58 · 1:10,000

KEY

- Red line (site boundary)
- 1 km from red line
- Green Belt
- Woodland (National Forest Inventory)
- Priority habitat inventory
- Flood Zone 2 / 3
- Surface water flooding (1% AEP)
- Ancient woodland
- Special Protection Area
- Site of Special Scientific Interest
- Local Nature Reserve
- Conservation area
- Statutory main river
- Listed building

FINDINGS

15 layers present · 12 none found · 3 not assessed

Within the red line: SSSI Impact Risk Zone, Local Nature Reserve, Ancient woodland, Priority habitat inventory, Woodland (National Forest Inventory), Green Belt, Agricultural land classification.

Surface water flooding (1% AEP): Not on the red line; nearest 33 m N; 0.8 ha within 250 m.

Special Protection Area: Thames Basin Heaths, 222 m N.

Site of Special Scientific Interest: Ockham and Wisley Commons SSSI, 222 m N.

Flood Zone 2 / 3: Flood Zone 2, 329 m SW.

Full schedule overleaf.

SCREENING ONLY

Statutory and published datasets only. Not a records-centre search, field survey or legal advice. Search radii are product defaults, not regulatory thresholds.

Data read live 25 Oct 2026: Natural England, Environment Agency, Historic England, Forestry Commission, Defra, local planning authorities via planning.data.gov.uk. Contains public sector information licensed under the Open Government Licence v3.0.

Former Wisley Airfield / Three Farms Meadows, Ockham

Layer	Searched	What the published data shows
INTERNATIONAL DESIGNATIONS		
Special Area of Conservation	10 km	Mole Gap to Reigate Escarpment, 7.5 km SE; Thursley, Ash, Pirbright & Chobham, 10.0 km NW.
Special Protection Area	10 km	Thames Basin Heaths, 222 m N.
Ramsar site	10 km	None found within 10 km of the red line.
NATIONAL DESIGNATIONS		
Site of Special Scientific Interest	2 km	Ockham and Wisley Commons SSSI, 222 m N.
National Nature Reserve	2 km	None found within 2 km of the red line.
SSSI Impact Risk Zone	red line	The red line falls in 3 impact risk zones (IRZ codes 0111242322231, 3111211211121, 3111241211121). Check the consultation criteria for the proposal type at irz.geodata.org.uk. Note: Reported only where the red line falls inside a zone. Check the zone's consultation criteria for the proposal type.
HABITATS AND NATURE RECOVERY		
Local Nature Reserve	2 km	Ockham and Wisley, within the red line.
Ancient woodland	2 km	Ancient semi-natural woodland (33 parcels), within the red line.
Priority habitat inventory	2 km	Within the red line: Deciduous woodland 0.5 ha. Within 2 km: Deciduous woodland 284 ha, Additional habitats only (no main habitat) 123 ha, Lowland heathland 60 ha, Good quality semi improved grassland 7.2 ha, Traditional orchard 1.7 ha.
GCN strategic opportunity area	2 km	None found within 2 km of the red line.
Nature improvement area	2 km	None found within 2 km of the red line.
Local nature recovery strategy area	2 km	Not assessed — data could not be retrieved. Reason: the publisher's dataset is empty nationally (planning.data 'local-nature-recovery-strategy' returned 0 records anywhere in England), so nothing was checked
Nutrient neutrality catchment	red line	None found within the red line. Note: Reported only where the red line falls inside one.
Woodland (National Forest Inventory)	1 km	Within the red line: Broadleaved 0.5 ha. Within 1 km: Broadleaved 61 ha, Conifer 34 ha, Felled 29 ha, Mixed mainly broadleaved 2.3 ha.
Common land and village green	1 km	Not assessed — data could not be retrieved. Reason: the publisher's dataset is empty nationally (planning.data 'common-land-and-village-green' returned 0 records anywhere in England), so nothing was checked
LANDSCAPE AND OPEN LAND		
National Landscape (AONB)	2 km	None found within 2 km of the red line.
National Park	2 km	None found within 2 km of the red line.
Green Belt	1 km	Guildford, within the red line; Elmbridge, 351 m E. Note: A national compilation by MHCLG from councils' yearly returns, not each council's adopted policies map. Confirm the boundary there before relying on it.
Local green space	1 km	Not assessed — data could not be retrieved. Reason: the publisher's dataset is empty nationally (planning.data 'local-green-space' returned 0 records anywhere in England), so nothing was checked
Agricultural land classification	red line	Grade 4, within the red line; Non Agricultural, within the red line. Note: Provisional 1:250,000 grades — not field survey. Reported for the red line only.
WATER AND FLOODING		
Flood Zone 2 / 3	1 km	Flood Zone 2, 329 m SW; Flood Zone 3, 450 m S.
Statutory main river	1 km	Stratford Brook, 459 m SW; Main river, 570 m S.

Former Wisley Airfield / Three Farms Meadows, Ockham

Layer	Searched	What the published data shows
WATER AND FLOODING		
Surface water flooding (1% AEP)	250 m	Not on the red line; nearest 33 m N; 0.8 ha within 250 m.
Flood storage area	1 km	None found within 1 km of the red line.
HERITAGE AND TREES		
Conservation area	1 km	Ockham, 366 m SW.
Listed building	500 m	Upton Farmhouse (Grade II), 426 m SE; Bridge End House (Grade II), 451 m SW; YARNE (Grade II), 488 m SE.
Scheduled monument	1 km	None found within 1 km of the red line.
Registered park and garden	1 km	None found within 1 km of the red line.
Tree preservation order (area)	250 m	None found within 250 m of the red line. Published data is incomplete for some councils — confirm locally.
Tree preservation order (tree)	250 m	None found within 250 m of the red line. Published data is incomplete for some councils — confirm locally.

How to read this schedule. 'None found' means the publisher was queried and returned nothing in the search radius. 'Not assessed' means the query failed — it is not a clear result. Layers supplied by local planning authorities (conservation areas, tree preservation orders, Green Belt, local green space) are not yet published by every council, so a nil return there must be confirmed with the council.

This sheet does not include protected or notable species records, local wildlife sites or other non-statutory designations held by local environmental records centres, which a Preliminary Ecological Appraisal normally requires. Distances are measured from the red line to the nearest edge of each feature in British National Grid. Data was read from each publisher at the moment the sheet was made (25 Oct 2026 19:58) and may have changed since.